COMPROBANTE DE INSCRIPCION CATASTRAL

REGISTRO NACIONAL
REPÚBLICA DE COSTA RICA

REGISTRO INMOBILIARIO
SUBDIRECCIÓN
CATASTRAL

INSCRIPCIÓN No:
2-2030585-2018

Fecha : 12/02/2018 13:58:44
Registrador: RONNY SALAZAR OBANDO
D5BBAB368F3C1076A3B0FC785D236AE5


Catastro Nacional
2018-9880-C
08/02/2018 08:39:07
Ingreso

cfia

Contrato 764940
Fecha 07/02/2018
Sellado CFIA

ENTERO: 253741556

SECCION DE PROPIEDAD EN CONDOMINIO

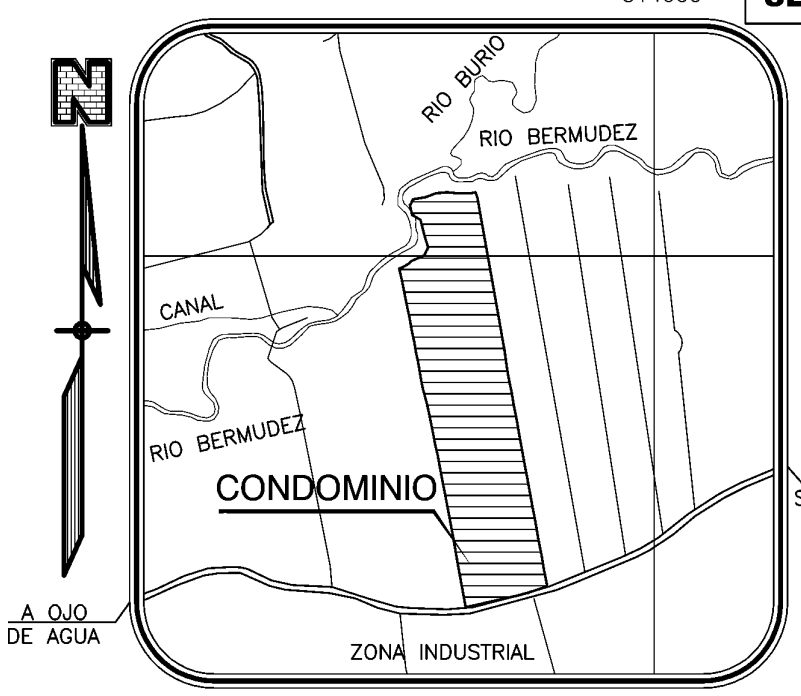

NOTAS GENERALES:

>TODAS LAS MEDIDAS Y DISTANCIAS ESTAN DADAS EN METROS.

>SE DESARROLLA BAJO EL REGIMEN DE PROPIEDAD EN CONDOMINIO.

>NUMERO DE PLANO DE CATASTRO DE FINCA MADRE A-1257557-2008.

>LOS PUNTOS P, N, T, SON VERTICES DE LA FINCA MATRIZ.

>FINCA FILIAL DESTINADA A USO INDUSTRIAL, BODEGAS, OFIBODEGAS Y OFICINAS.

>DISTANCIA FRENTE A ACCESO VEHICULAR 2 AC DEL VERTICE N°4 AL VERTICE N°5 ES DE 57.80m.

>PUNTO PI CORRESPONDE CON LA INTERSECCION DE CALLES PUBLICAS

DERROTERO

LINEA	A Z I M U T	DISTANCIA
1-2	74°20'29"	15.83
2-3	349°24'29"	24.47
3-4	79°24'29"	5.41
4-5	349°26'20"	57.80
5-6	270°37'52"	36.51
6-7	259°32'04"	27.15
7-8	169°56'24"	6.42
8-9	169°51'20"	35.13
9-10	169°49'31"	48.53
10-1	80°25'32"	42.45

NOTAS DE LEVANTAMIENTO:

> LEVANTAMIENTO POLAR.
> POLIGONAL CERRADA.
> ERROR ANGULAR 00°01'.
> ERROR LINEAL 0.01m.

NOTAS DE SIMBOLOGIA:

> FFM= FINCA FILIAL MATRIZ
> AC= AREA COMUN
> AP= AREA DE PASO AC
> ZV= ZONA VERDE AC
> H= DEPOSITO DE BASURA AC
> C= CASETA DE GUARDA AC
> ACC= ACCESO VEHICULAR AC
> EST= ESTACIONAMIENTOS AC
> SPLT= SERVIDUMBRE DE PASO LINEA DE TRANSMISION AC
> LFM= LINDERO DE FINCA MATRIZ
> M= CUARTO DE MANTENIMIENTO AC
> LR= LAGUNA DE RETENCION AC
> ZPR= ZONA DE PROTECCION RIO AC
> PT= PLANTA DE TRATAMIENTO AC

UBICACION GEOGRAFICA

HOJAS CARTOGRAFICAS COCO – LINDORA

ESCALA 1:10000

NOTA DE AREAS COMUNES:


> TODAS LAS AREAS COMUNES SON PROPIEDAD DE LOS CONDOMINOS DEL ANTEPROYECTO CONDOMINIO CUBO PARK INDUSTRIAL Y DE BODEGAS DE FINCAS FILIALES MATRICES.

NOTA DE APC:

>EL DISEÑO DE SITIO DEL PROYECTO FUE TRAMITADO EN EL SISTEMA APC BAJO EL NUMERO DE CONTRATO OC-758173.


NOTA DE COLINDANTES:

> Ⓐ = MISAEL VENEGAS RODRIGUEZ
> Ⓑ = RODOLFO ALFARO MURILLO

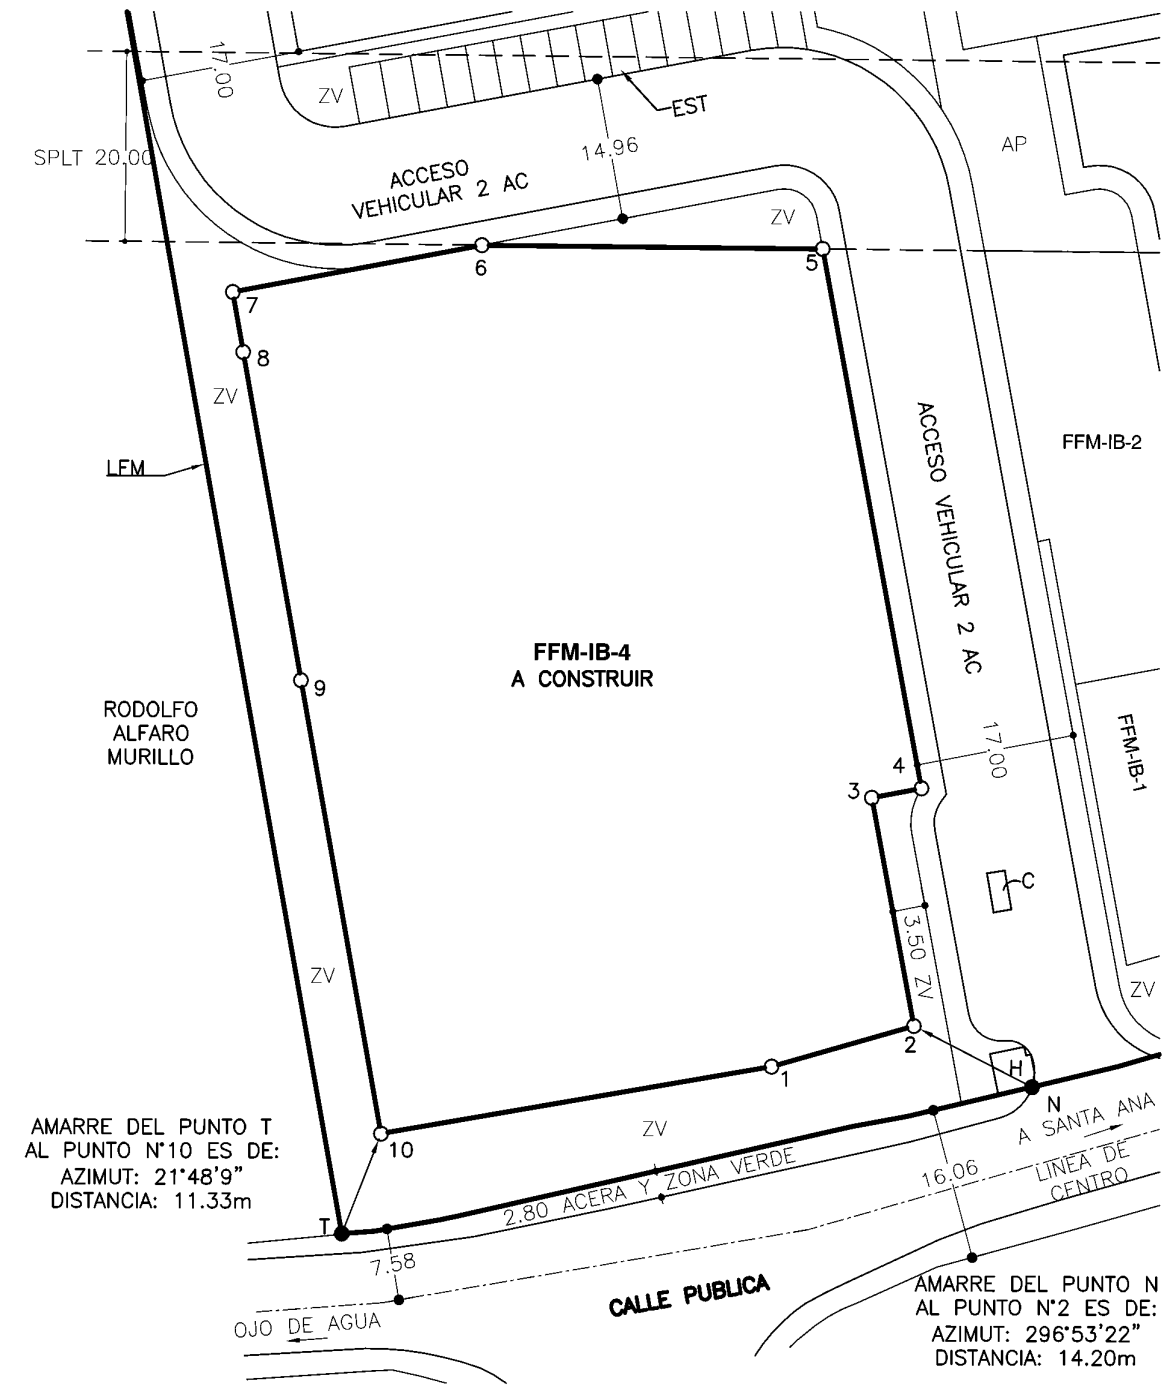

DETALLE DE FINCA FILIAL A CATASTRAR

ESCALA 1:750

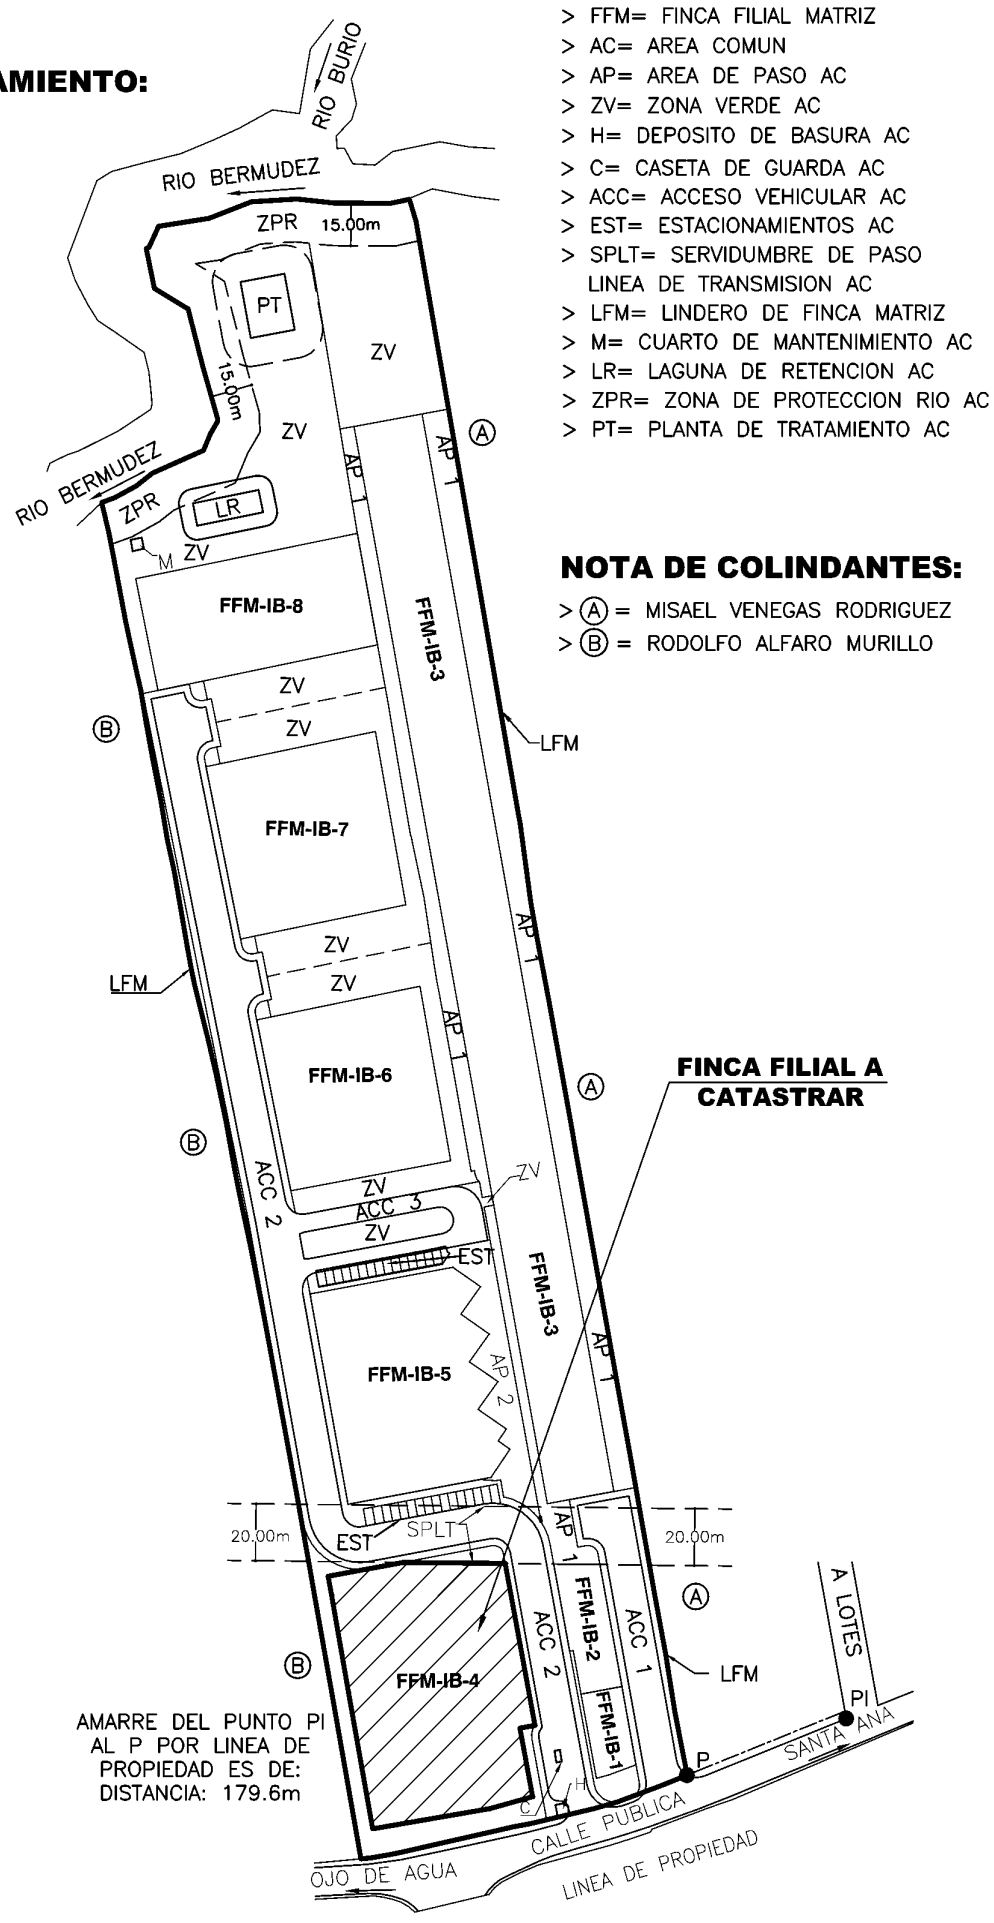

DISEÑO DE CONDOMINIO

ESCALA 1:2500

FFM-IB-4

ANTEPROYECTO CONDOMINIO CUBO PARK INDUSTRIAL Y DE BODEGAS DE FINCAS FILIALES MATRICES	ESCALA: INDICADA FECHA: ENERO 2018	AREA: **5452m²**	SITUADO EN: SAN RAFAEL DISTRITO: 08° SAN RAFAEL CANTON: 01° ALAJUELA PROVINCIA: 02° ALAJUELA	FINCA MATRIZ: FOLIO REAL N°2004505M-000 FINCA FILIAL FOLIO REAL N°2171791F-000
TOPOGRAFO ASOCIADO: RAMON RAMIREZ CAÑAS T.A. 1030	PROTOCOLO TOMO: 20756 FOLIO: 004	AREA SEGUN REGISTRO PUBLICO: FINCA MATRIZ: 67111.58m² FINCA FILIAL: 5452.30m²		