COMPROBANTE DE INSCRIPCION CATASTRAL

REGISTRO NACIONAL
REPÚBLICA DE COSTA RICA

REGISTRO INMOBILIARIO
SUBDIRECCIÓN
CATASTRAL

INSCRIPCIÓN No:
2-2030584-2018

Fecha : 12/02/2018 13:58:12
Registrador: RONNY SALAZAR OBANDO
7607840B30E0872F7511C99AD9AB7FEB


Catastro Nacional
2018-9879-C
08/02/2018 08:38:59
Ingreso

cfia

Contrato 764940
Fecha 07/02/2018
Sellado CFIA

ENTERO: 253741106

SECCION DE PROPIEDAD EN CONDOMINIO

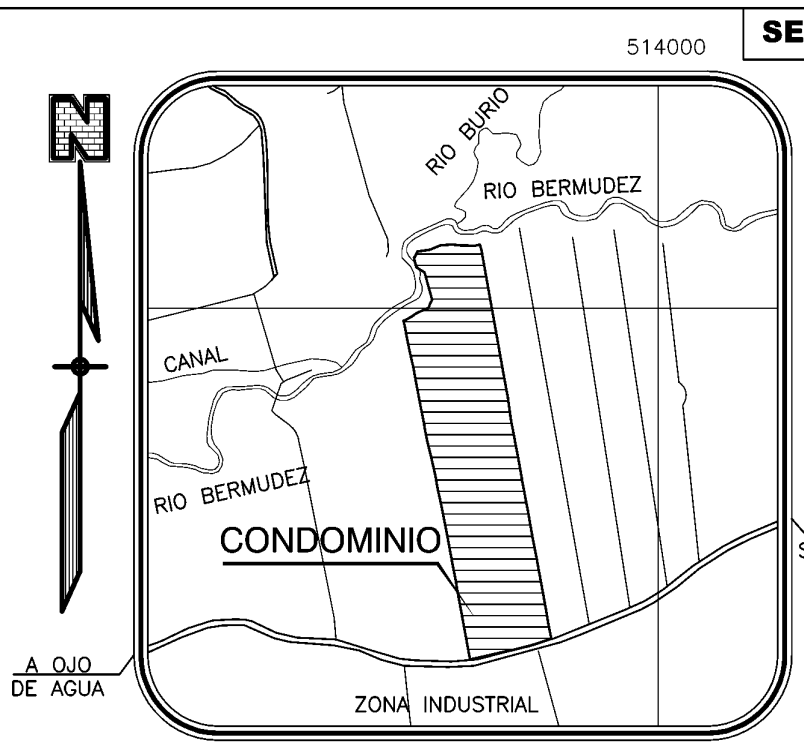

NOTAS GENERALES:

>TODAS LAS MEDIDAS Y DISTANCIAS ESTAN DADAS EN METROS.

>SE DESARROLLA BAJO EL REGIMEN DE PROPIEDAD EN CONDOMINIO.

>NUMERO DE PLANO DE CATASTRO DE FINCA MADRE A-1257557-2008.

>LOS PUNTOS P, T, SON VERTICES DE LA FINCA MATRIZ.

>FINCA FILIAL DESTINADA A USO INDUSTRIAL, BODEGAS, OFIBODEGAS Y OFICINAS.

>DISTANCIA FRENTE A ACCESO VEHICULAR 2 AC DEL VERTICE N°8 AL VERTICE N°10 ES DE 75.17m.

>DISTANCIA FRENTE A AREA DE PASO AC DEL VERTICE N°11 AL VERTICE N°8 ES DE 159.07m.

>PUNTO PI CORRESPONDE CON LA INTERSECCION DE CALLES PUBLICAS

DERROTERO

LINEA	A Z I M U T	DISTANCIA
1-2	36°04'52"	12.06
2-3	304°18'18"	12.28
3-4	35°44'51"	12.05
4-5	304°30'34"	12.29
5-6	36°03'54"	11.99
6-7	304°18'47"	12.02
7-8	259°38'44"	51.85
8-9	169°36'21"	44.74
9-10	169°35'10"	30.43
10-11	79°31'20"	51.96
11-12	34°30'34"	11.98
12-13	304°30'34"	5.11
13-14	34°30'34"	5.14
14-1	304°18'18"	12.30

UBICACION GEOGRAFICA
HOJAS CARTOGRAFICAS COCO – LINDORA
ESCALA 1:10000

NOTA DE AREAS COMUNES:

> TODAS LAS AREAS COMUNES SON PROPIEDAD DE LOS CONDOMINOS DEL ANTEPROYECTO CONDOMINIO CUBO PARK INDUSTRIAL Y DE BODEGAS DE FINCAS FILIALES MATRICES.

NOTA DE COLINDANTES:


> Ⓐ = MISAEL VENEGAS RODRIGUEZ
> Ⓑ = RODOLFO ALFARO MURILLO

NOTA DE APC:


>EL DISEÑO DE SITIO DEL PROYECTO FUE TRAMITADO EN EL SISTEMA APC BAJO EL NUMERO DE CONTRATO OC-758173.

NOTAS DE LEVANTAMIENTO:

> LEVANTAMIENTO POLAR.
> POLIGONAL CERRADA.
> ERROR ANGULAR 00°01'.
> ERROR LINEAL 0.01m.

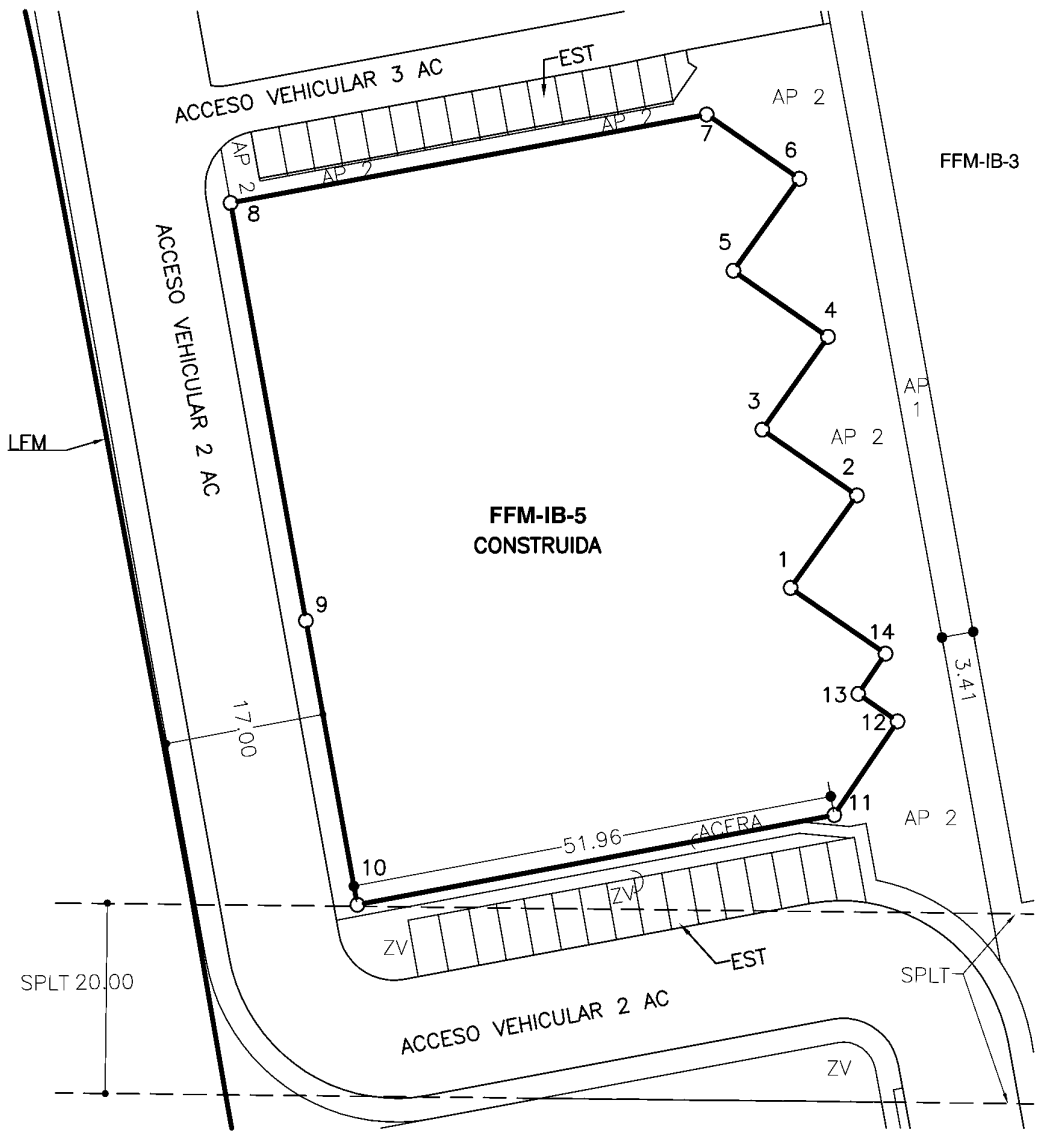

DETALLE DE FINCA FILIAL A CATASTRAR
ESCALA 1:750

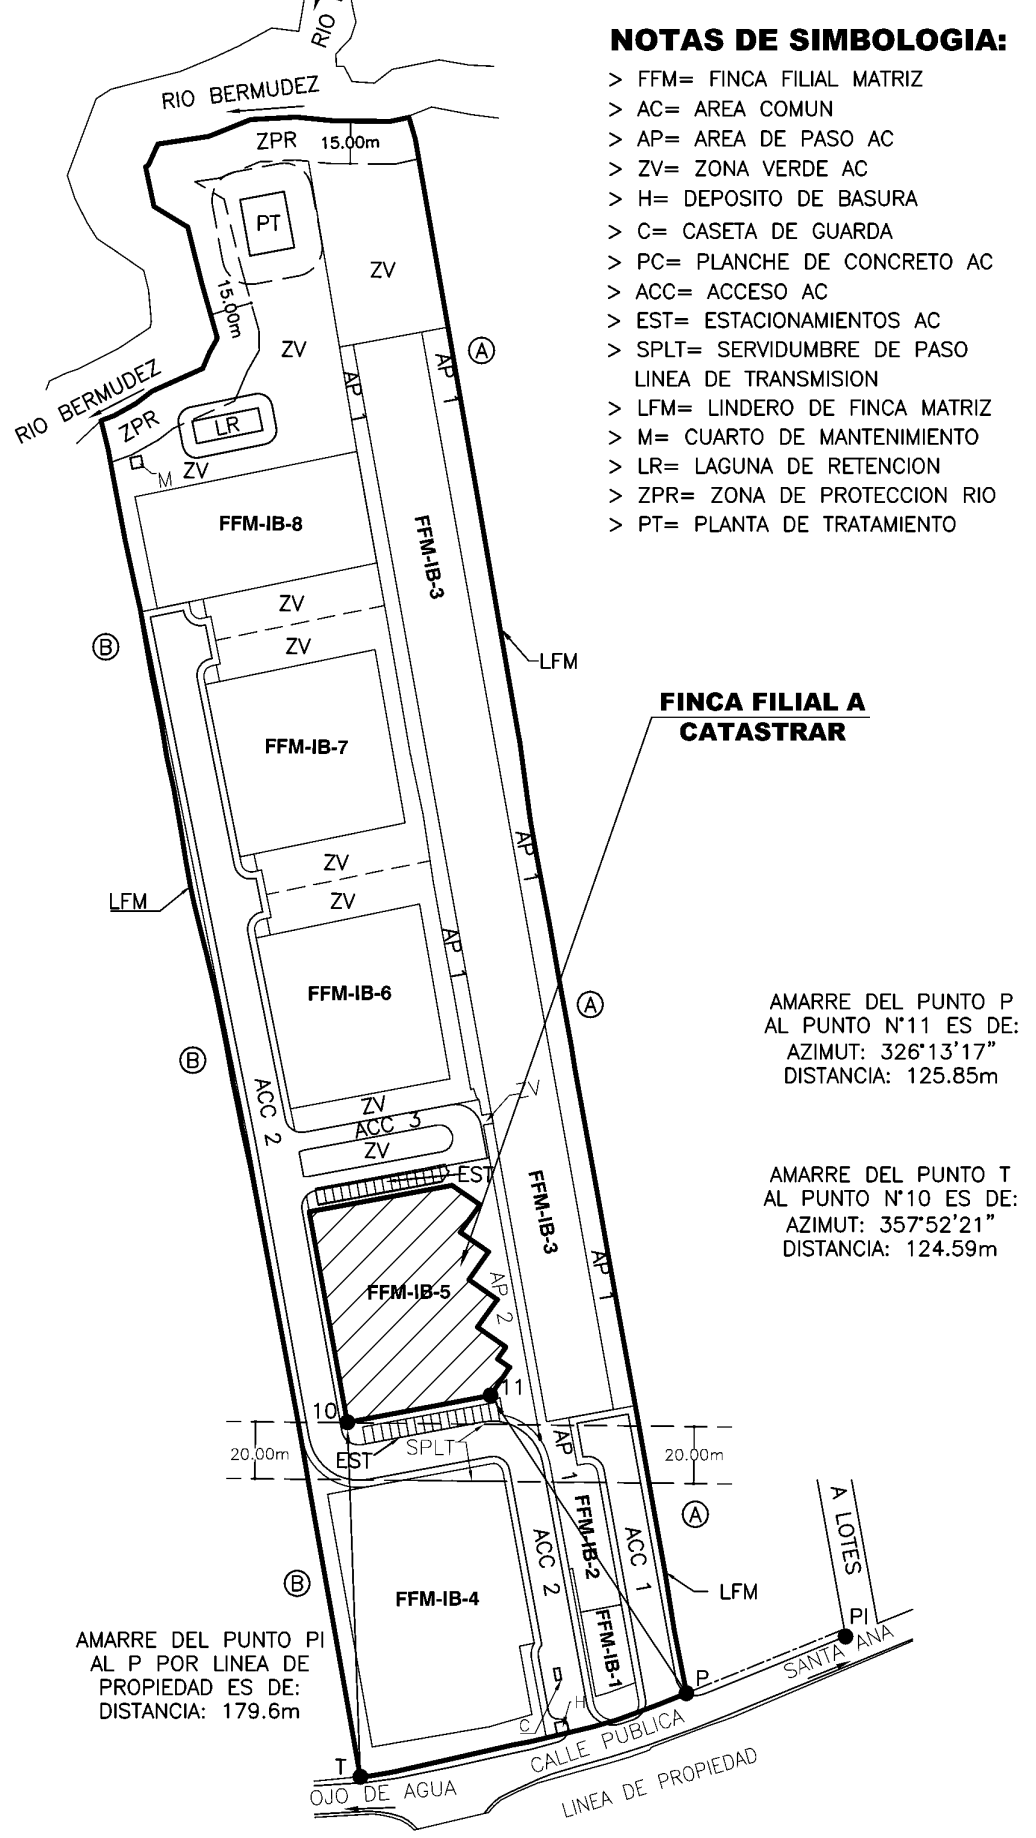

DISEÑO DE CONDOMINIO
ESCALA 1:2500

NOTAS DE SIMBOLOGIA:

> FFM= FINCA FILIAL MATRIZ
> AC= AREA COMUN
> AP= AREA DE PASO AC
> ZV= ZONA VERDE AC
> H= DEPOSITO DE BASURA
> C= CASETA DE GUARDA
> PC= PLANCHE DE CONCRETO AC
> ACC= ACCESO AC
> EST= ESTACIONAMIENTOS AC
> SPLT= SERVIDUMBRE DE PASO LINEA DE TRANSMISION
> LFM= LINDERO DE FINCA MATRIZ
> M= CUARTO DE MANTENIMIENTO
> LR= LAGUNA DE RETENCION
> ZPR= ZONA DE PROTECCION RIO
> PT= PLANTA DE TRATAMIENTO

FFM-IB-5

ANTEPROYECTO CONDOMINIO CUBO PARK INDUSTRIAL Y DE BODEGAS DE FINCAS FILIALES MATRICES	ESCALA: INDICADA FECHA: ENERO 2018	AREA: **4231m²**	SITUADO EN: SAN RAFAEL DISTRITO: 08° SAN RAFAEL CANTON: 01° ALAJUELA PROVINCIA: 02° ALAJUELA	FINCA MATRIZ: FOLIO REAL N°2004505M-000 FINCA FILIAL FOLIO REAL N°2171792F-000
TOPOGRAFO ASOCIADO: RAMON RAMIREZ CAÑAS T.A. 1030	PROTOCOLO TOMO: 20756 FOLIO: 004	AREA SEGUN REGISTRO PUBLICO: FINCA MATRIZ: 67111.58m² FINCA FILIAL: 4230.89m²		