COMPROBANTE DE INSCRIPCION CATASTRAL

REGISTRO NACIONAL
REPÚBLICA DE COSTA RICA

REGISTRO INMOBILIARIO
SUBDIRECCIÓN
CATASTRAL

INSCRIPCIÓN No:
2-2030582-2018


Fecha : 12/02/2018 13:57:03
Registrador: RONNY SALAZAR OBANDO
338CE0F8A8367F6244951DFAF7E94159

Catastro Nacional
2018-9875-C
08/02/2018 08:38:30
Ingreso

cfia
Contrato 764940
Fecha 07/02/2018
Sellado CFIA

ENTERO: 253741262

SECCION DE PROPIEDAD EN CONDOMINIO

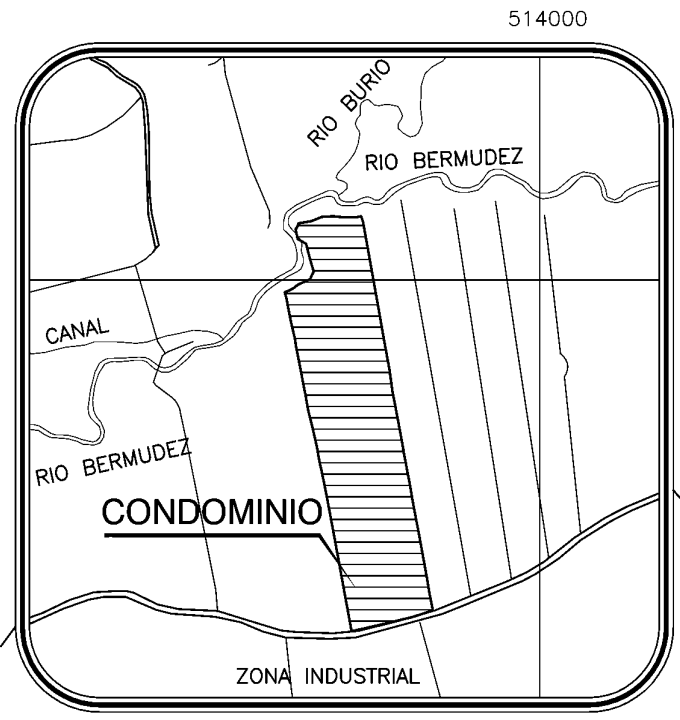

DERROTERO

LINEA	A Z I M U T	DISTANCIA
1–2	78°29'38"	60.24
2–3	349°53'36"	61.82
3–4	258°29'38"	61.75
4–1	168°29'38"	61.80

NOTAS DE SIMBOLOGIA:

> FFM= FINCA FILIAL MATRIZ
> AC= AREA COMUN
> AP= AREA DE PASO AC
> ZV= ZONA VERDE AC
> H= DEPOSITO DE BASURA AC
> C= CASETA DE GUARDA AC
> ACC= ACCESO VEHICULAR AC
> EST= ESTACIONAMIENTOS AC
> SPLT= SERVIDUMBRE DE PASO LINEA DE TRANSMISION AC
> LFM= LINDERO DE FINCA MATRIZ
> M= CUARTO DE MANTENIMIENTO AC
> LR= LAGUNA DE RETENCION AC
> ZPR= ZONA DE PROTECCION RIO AC
> PT= PLANTA DE TRATAMIENTO AC

NOTAS DE LEVANTAMIENTO:

> LEVANTAMIENTO POLAR.
> POLIGONAL CERRADA.
> ERROR ANGULAR 00°01'.
> ERROR LINEAL 0.01m.

NOTA DE AREAS COMUNES:

> TODAS LAS AREAS COMUNES SON PROPIEDAD DE LOS CONDOMINOS DEL ANTEPROYECTO CONDOMINIO CUBO PARK INDUSTRIAL Y DE BODEGAS DE FINCAS FILIALES MATRICES.

NOTAS GENERALES:

>TODAS LAS MEDIDAS Y DISTANCIAS ESTAN DADAS EN METROS.

>SE DESARROLLA BAJO EL REGIMEN DE PROPIEDAD EN CONDOMINIO.

>NUMERO DE PLANO DE CATASTRO DE FINCA MADRE A–1257557–2008.

>LOS PUNTOS P, T, SON VERTICES DE LA FINCA MATRIZ.

>FINCA FILIAL DESTINADA A USO INDUSTRIAL, BODEGAS, OFIBODEGAS Y OFICINAS.

>DISTANCIA FRENTE A ACCESO VEHICULAR 2 AC DEL VERTICE N°4 AL VERTICE N°1 ES DE 61.80m.

>PUNTO PI CORRESPONDE CON LA INTERSECCION DE CALLES PUBLICAS

UBICACION GEOGRAFICA

HOJAS CARTOGRAFICAS COCO – LINDORA


ESCALA 1:10000

NOTA DE APC:

>EL DISEÑO DE SITIO DEL PROYECTO FUE TRAMITADO EN EL SISTEMA APC BAJO EL NUMERO DE CONTRATO OC–758173.


NOTA DE COLINDANTES:

> (A) = MISAEL VENEGAS RODRIGUEZ
> (B) = RODOLFO ALFARO MURILLO

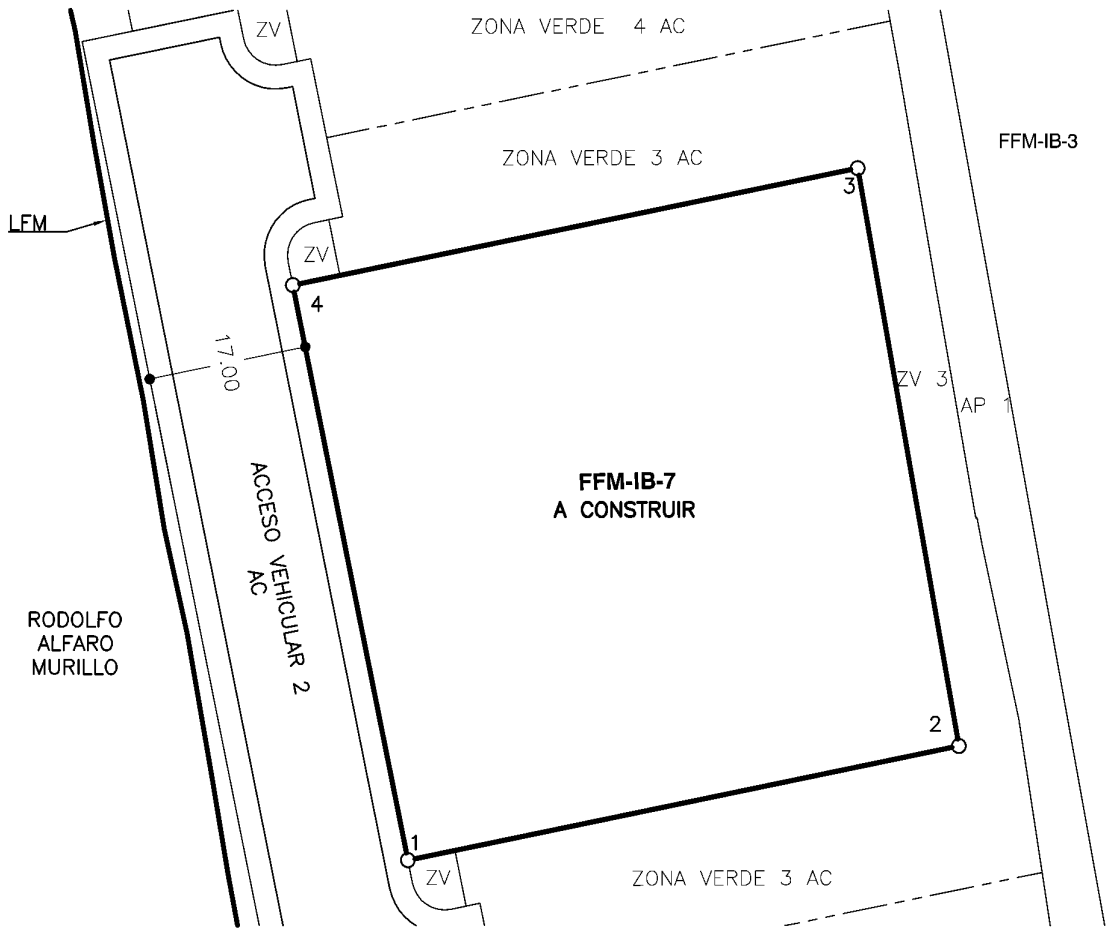

DETALLE DE FINCA FILIAL A CATASTRAR

ESCALA 1:750

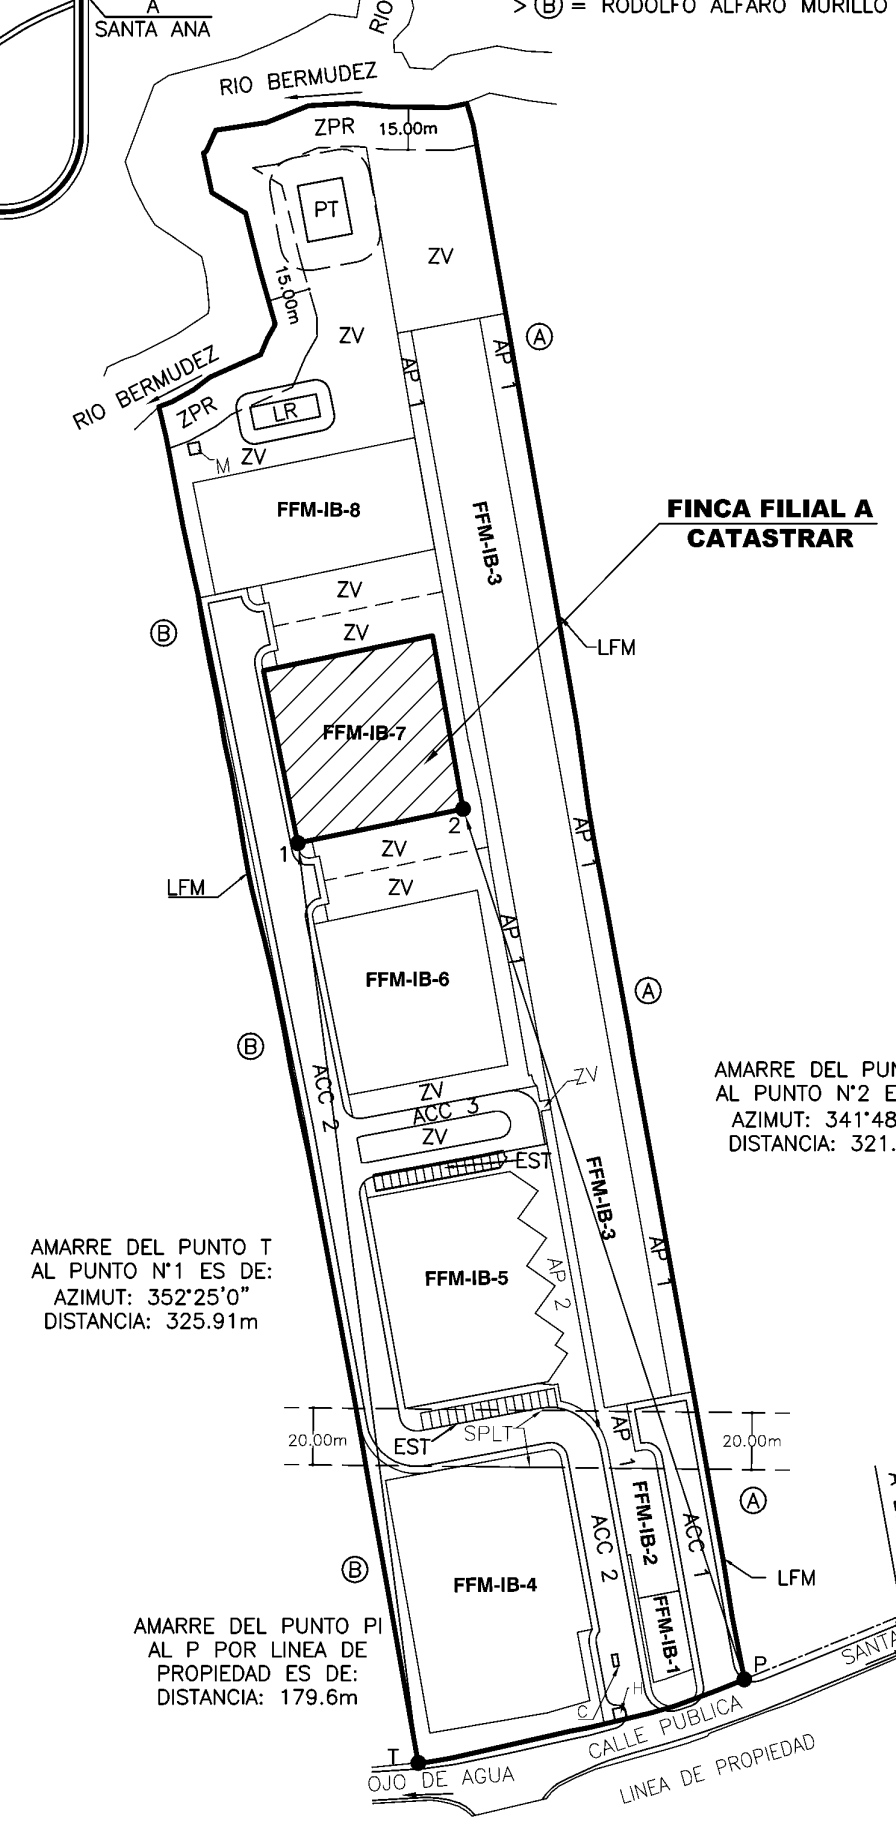

DISEÑO DE CONDOMINIO

ESCALA 1:2500

FFM-IB-7

ANTEPROYECTO CONDOMINIO CUBO PARK INDUSTRIAL Y DE BODEGAS DE FINCAS FILIALES MATRICES	ESCALA: INDICADA FECHA: ENERO 2018	AREA: **3770m²**	SITUADO EN: SAN RAFAEL DISTRITO: 08° SAN RAFAEL CANTON: 01° ALAJUELA PROVINCIA: 02° ALAJUELA	FINCA MATRIZ: FOLIO REAL N°2004505M–000 FINCA FILIAL FOLIO REAL N°2171794F–000
TOPOGRAFO ASOCIADO: RAMON RAMIREZ CAÑAS T.A. 1030	PROTOCOLO TOMO: 20756 FOLIO: 004	AREA SEGUN REGISTRO PUBLICO: FINCA MATRIZ: 67111.58m² FINCA FILIAL: 3769.60m²		